






CARRERE SAS
391 route de Gimont
32120 MAUVEZIN
Tél : 05.62.06.83.05

Commune de : MONCLAR SUR L'OSSE

Sécurisation et aménagements
de la traversée du village

VOIRIE / ASSAINISSEMENT
PLAN D'EXECUTION

Echelle : 1/200

N°CHANTIER	D	ADRESSE	MONCLAR SUR L'OSSE
INDICES	DATES	MODIFICATIONS	
A	29/07/2026	Création du document	
B	03/09/2026	Modification du document	

MAÎTRE D'OUVRAGE :

Maire de MONCLAR SUR L'OSSE
Au Village
32000 MONCLAR SUR L'OSSE

MAÎTRE D'OEUVRE :

XAGE
31 rue Mécabon
32000 FLEURANCE
Tél : 05.62.06.22.31